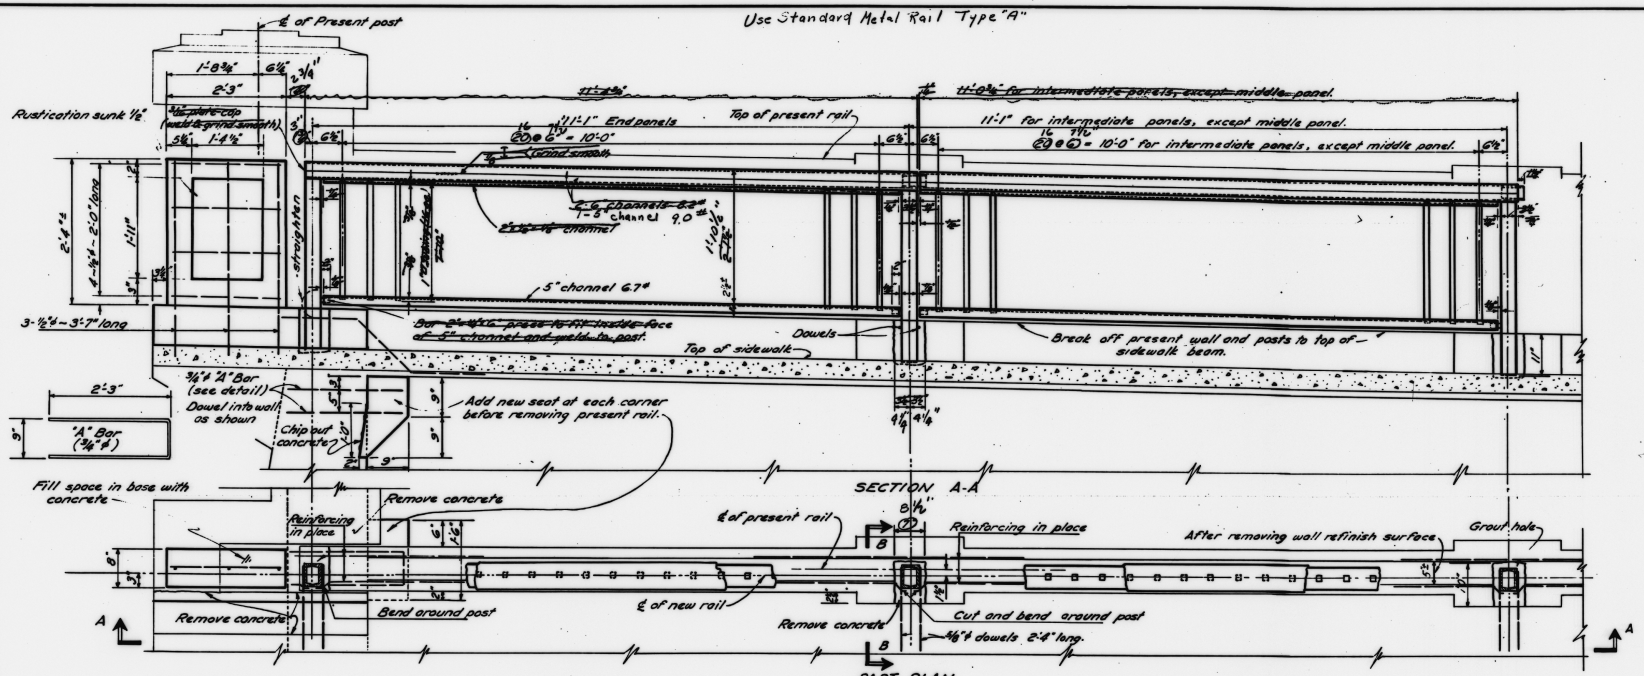



CITY OF RENO, NEVADA
DEPARTMENT OF ENGINEERING

**BOOTH STREET BRIDGE**
**RAILING DETAILS**

9.6.81

Sheet #2

VB-10-3